

חישוב כמויות

אזור מתקן

חישוב נפח ערימה

המדדה בוצעה בתאריך 2024/11/13


כמויות:

נפח ערימה עד לקרקע טבעית:

מ"ק 19,967.59

Cut/Fill Summary

Name	Cut Factor	Fill Factor	2d Area	Cut	Fill	Net
ערימה עד לקרקע טבעית	1.000	1.000	10892.99sq.m	9.70 Cu. M.	19967.59 Cu. M.	19957.89 Cu. M.<Fill>
Totals			10892.99sq.m	9.70 Cu. M.	19967.59 Cu. M.	19957.89 Cu. M.<Fill>

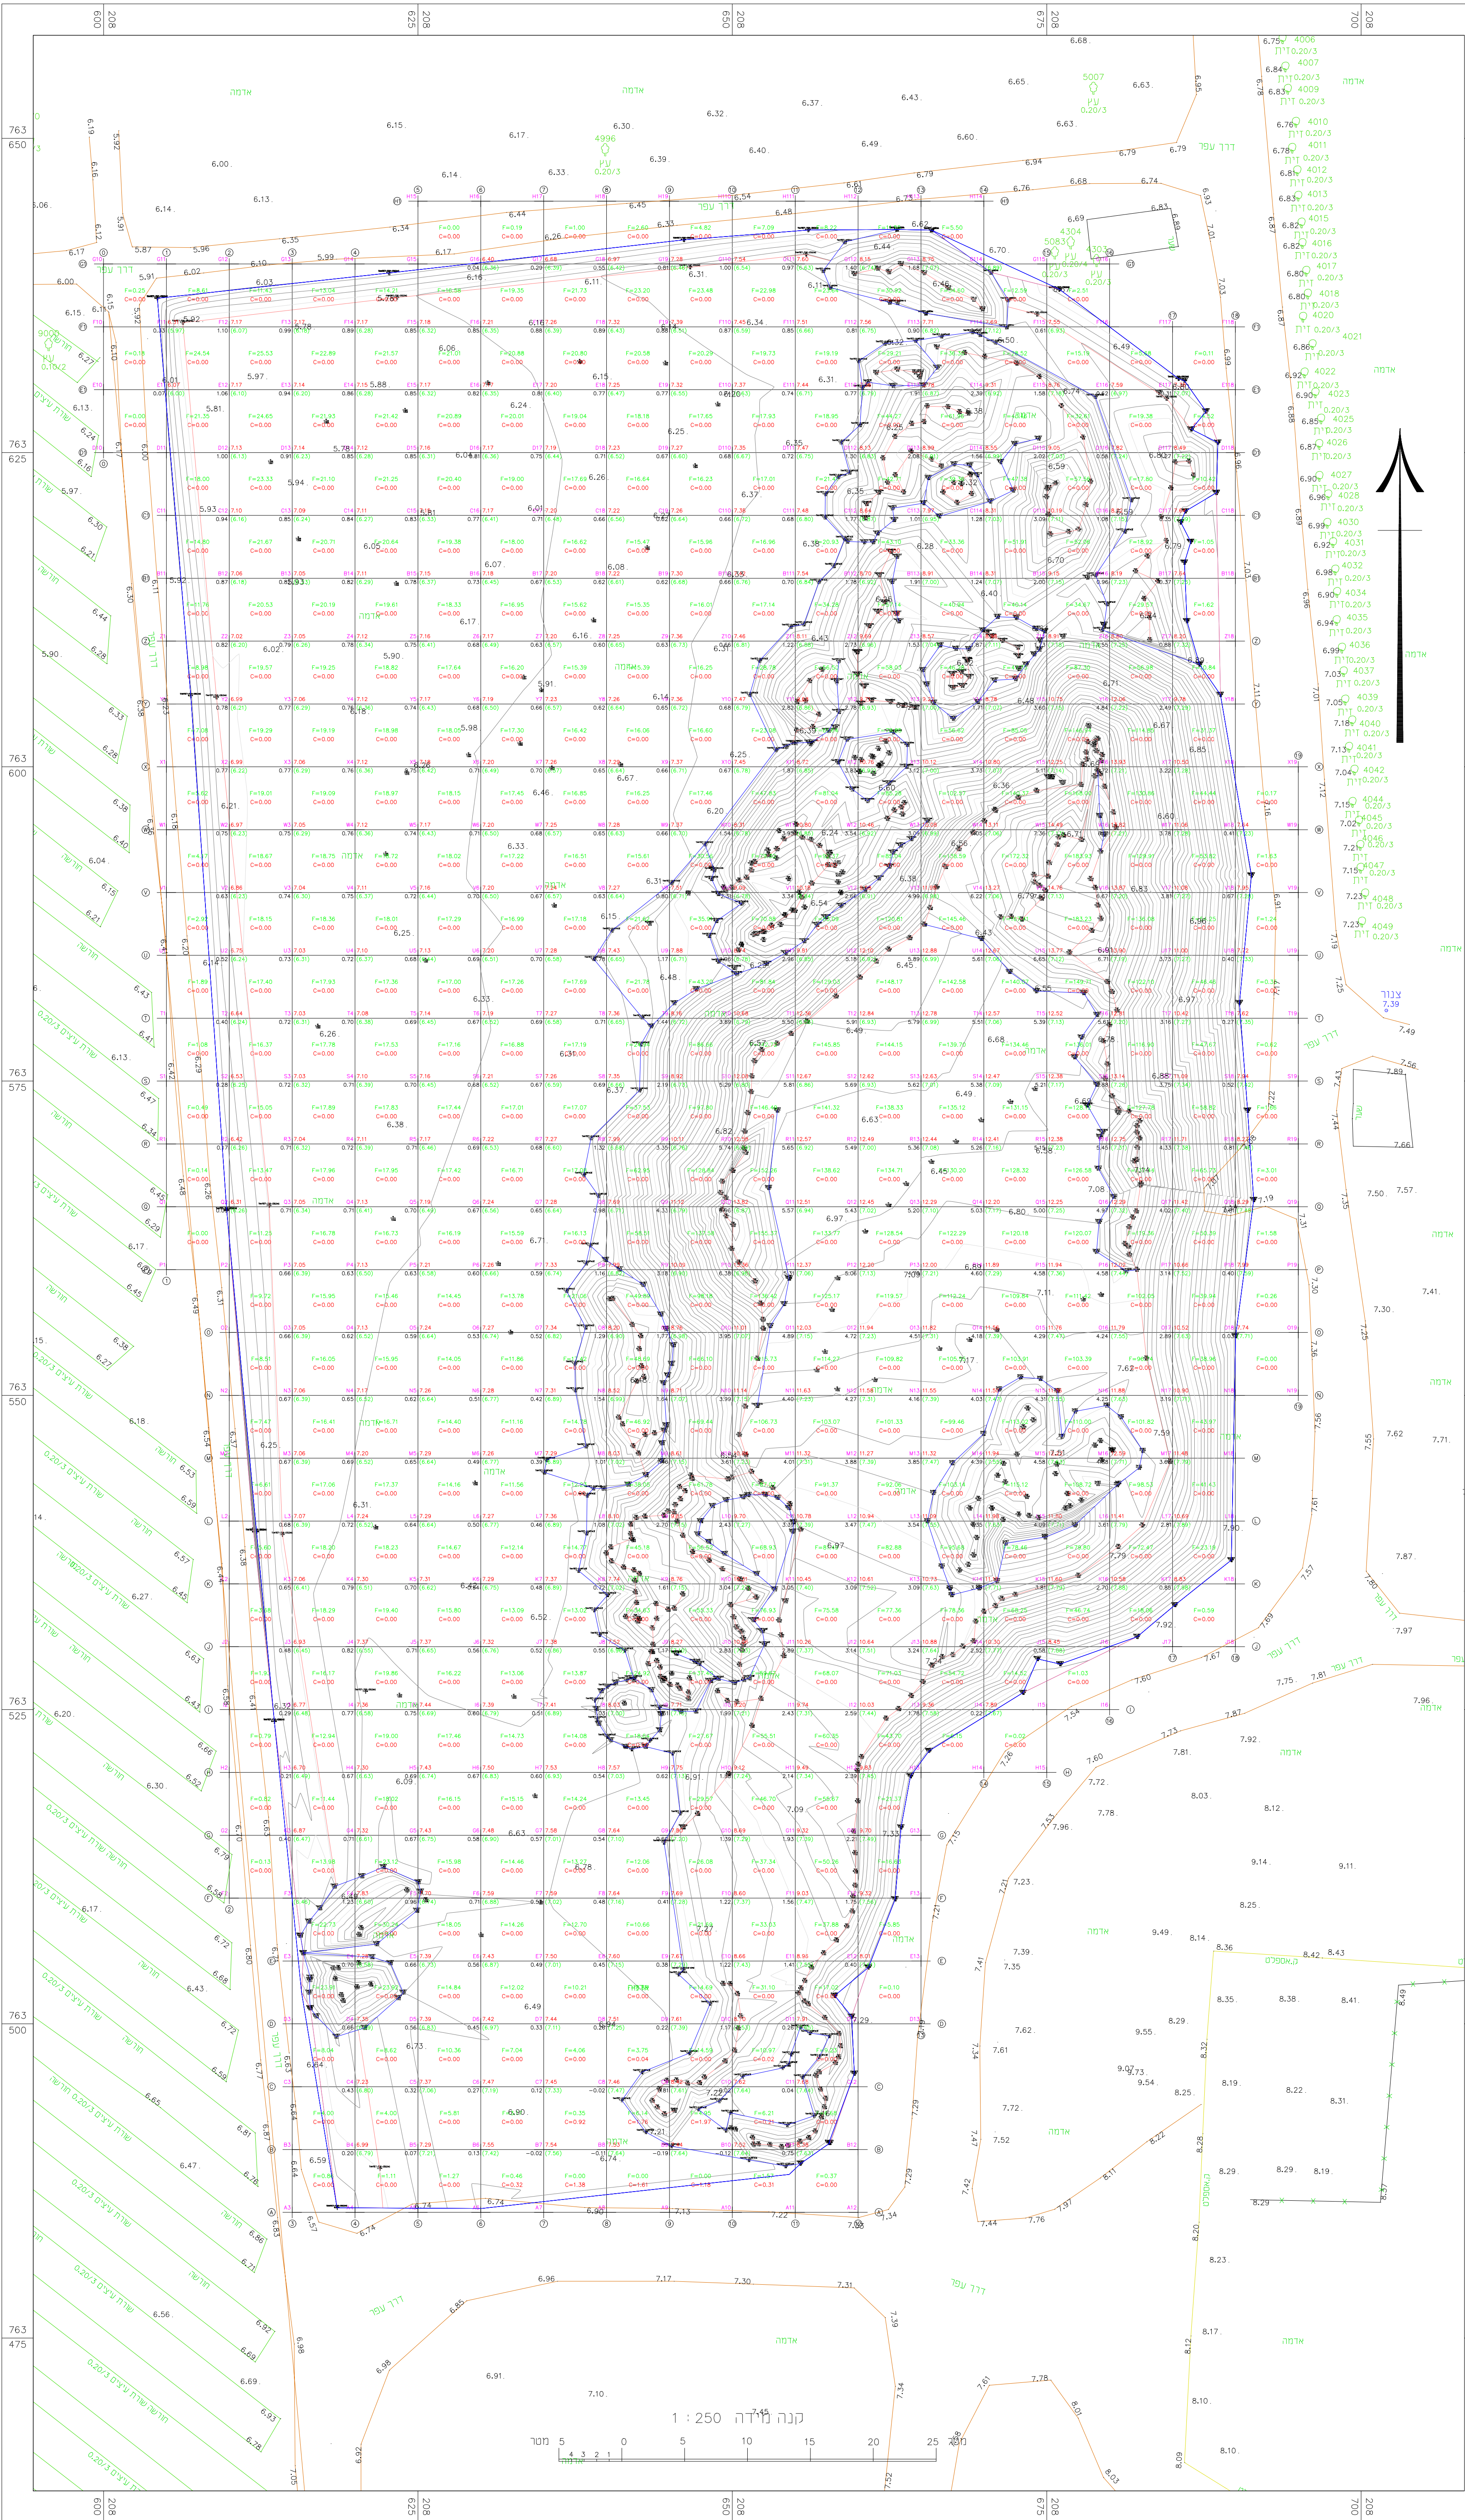

פרויקט: מתקן התפלה	שם:	תאריך:	חתימה:
	מורד:	13.11.2024	
שם תכנית: חישוב נפח ערימה	שרטוט:	17.11.2024	
	בקר:	18.11.2024	
מס' תכנית: 1	שם קובץ:	מחזור: 00	מס' עבודה: 1
מיקום קובץ:	קנה מידה: 1:250		